

NHÀ PHỐ 4,6 × 8,6 M

1 trệt · 2 lầu · 1 tum | Gara ô tô trong nhà | 3 phòng ngủ khép kín | Hiện đại, thông thoáng

39,56 m²

NGANG 4,60 M × DÀI 8,60 M

01

LỐI GIAO THÔNG

Cầu thang chữ U đặt lệch phải, xuyên suốt bốn tầng.

02

LẤY SÁNG

Giếng trời trên thang + cửa trước/sau tạo hiệu ứng ống khói.

03

RIỀNG TƯ

Không gian sinh hoạt nâng lên lầu 1; mỗi phòng ngủ có WC riêng.

04

MẶT TIỀN

Lam đứng, ban công cây xanh và cửa kính Low-E khung nhôm.


PHƯƠNG ÁN MẶT BẰNG

SƠ ĐỒ Ý TƯỞNG · KÍCH THƯỚC QUY ĐỔI THEO TỶ LỆ

00 / GROUND

TẦNG TRỆT

GARA · KHÁCH · THANG

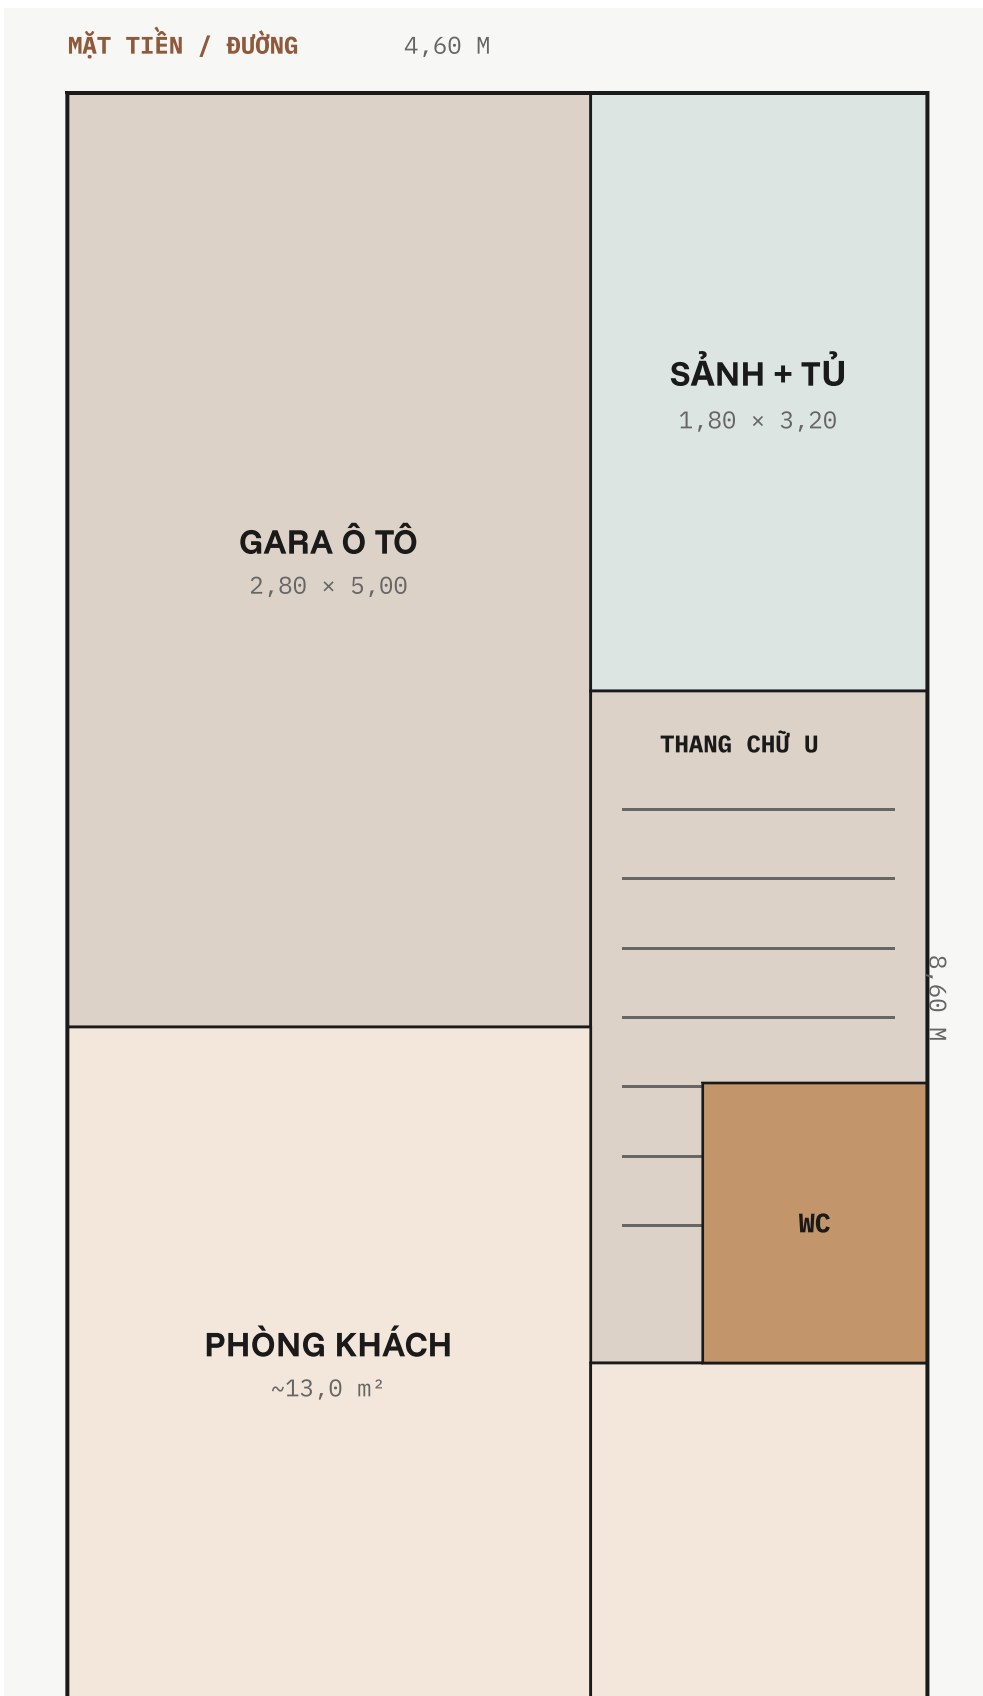

01 Khoảng ô tô 2,80 × 5,00 m; cửa cuốn nan thoáng và cửa đi riêng bên phải.

02 Phòng khách dạng chữ L ở cuối nhà, ngăn gara bằng vách kính kín khí.


03 WC nhỏ tận dụng dưới thang; tủ giày và kho kỹ thuật đặt dọc sảnh.

04 Cửa sau/ô thoáng cao kết hợp giếng trời trên thang để hút khí nóng.

01 / LEVEL

LẦU 1

BẾP · ĂN · MASTER

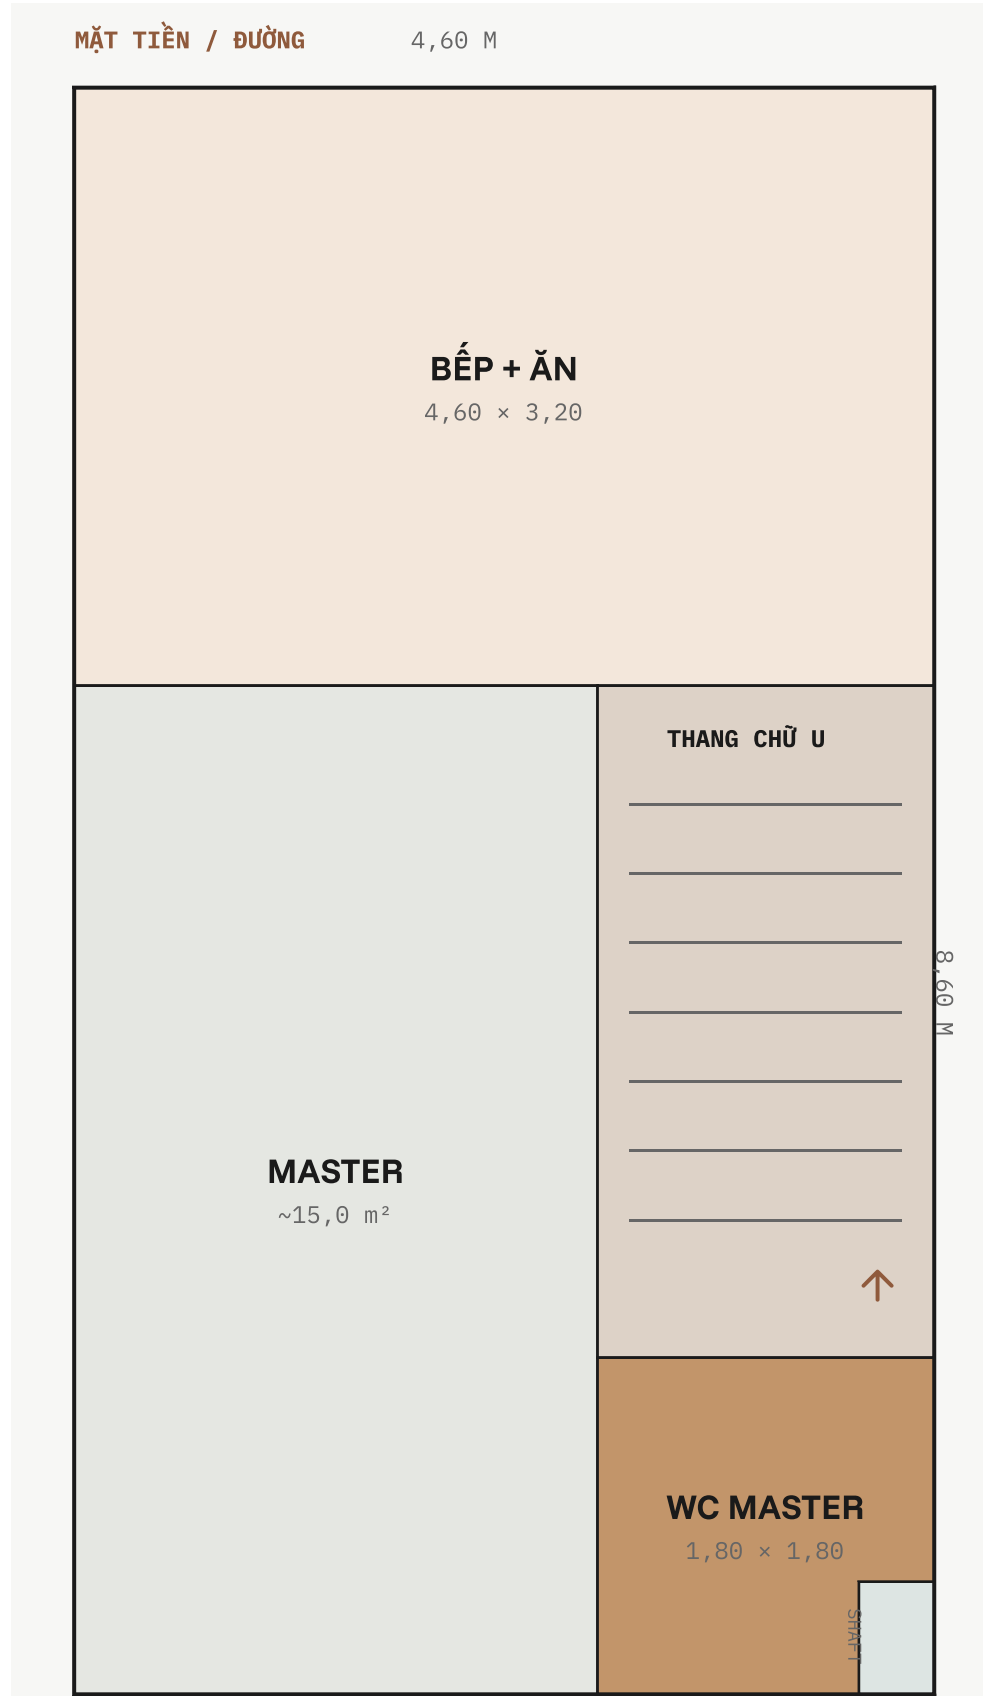

01 Bếp chữ L và bàn đảo/bàn ăn ở phía trước, mở ra ban công xanh.

02 Master nằm cuối nhà để yên tĩnh; giường queen, tủ áo âm tường.


03 WC master 1,80 × 1,80 m xếp chồng cùng trục kỹ thuật các tầng.

04 Vách kính trên ô thang đưa ánh sáng xuống sảnh và tầng trệt.

02 / LEVEL

LẦU 2

02 PHÒNG NGỦ · 02 WC

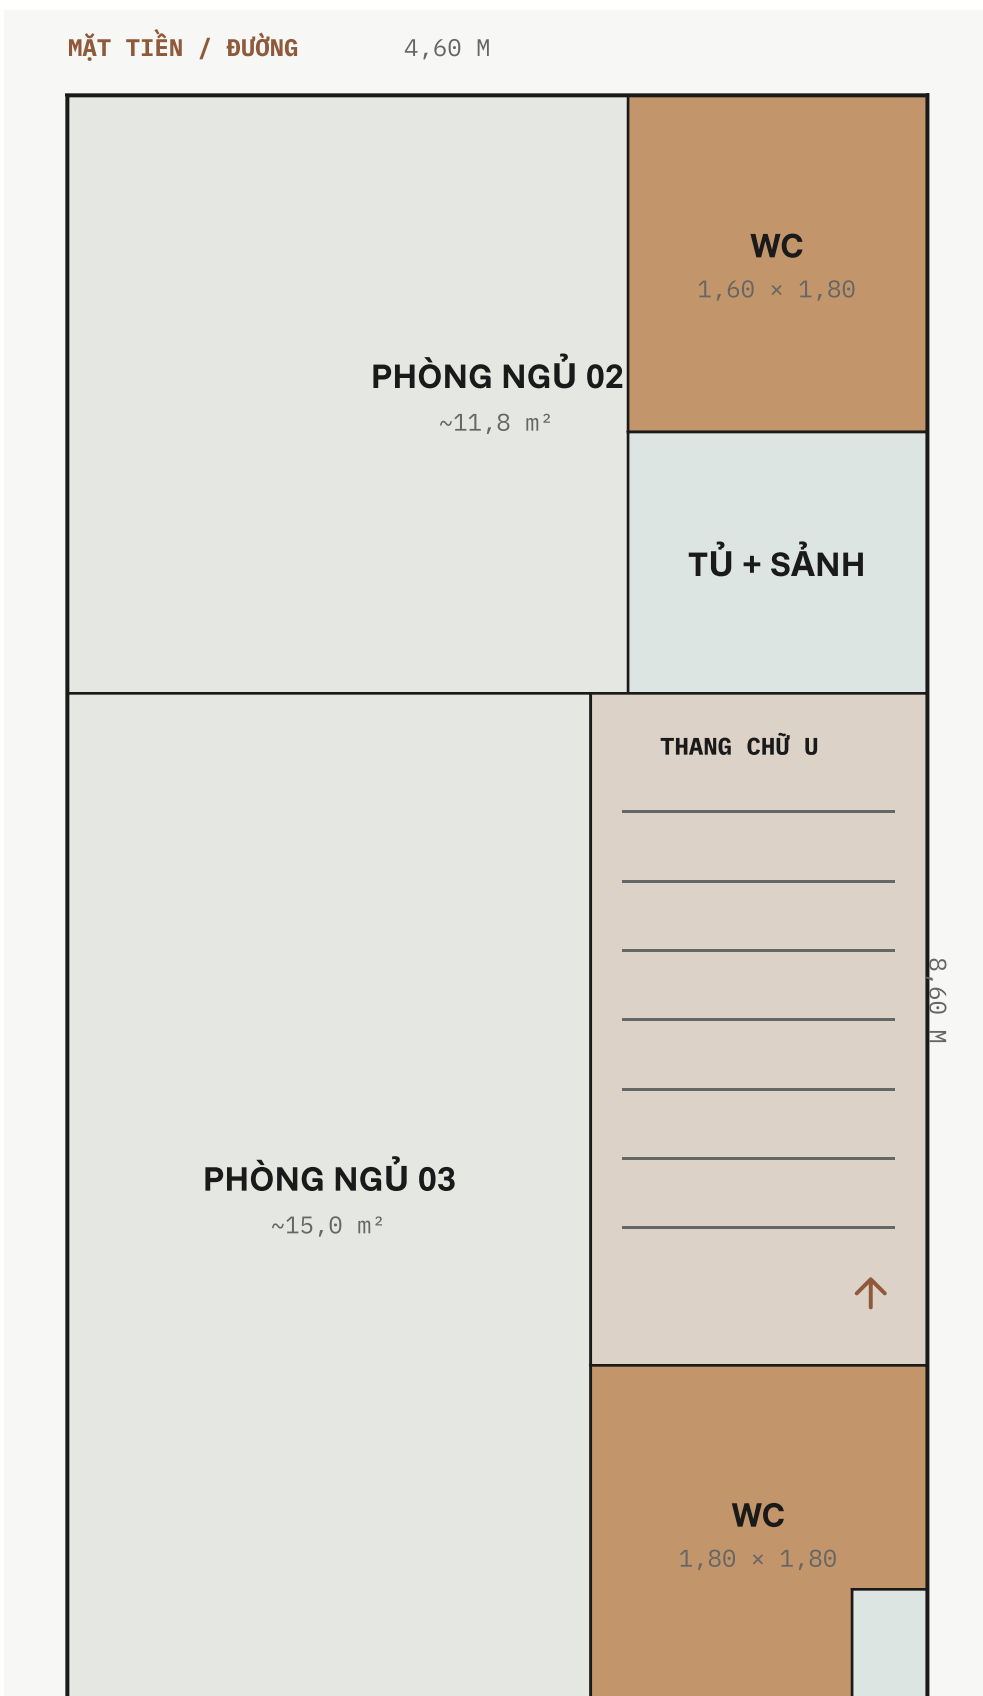

01 Phòng ngủ trước khoảng 11,8 m², có WC 1,60 × 1,80 m và cửa sổ lớn.

02 Phòng ngủ sau khoảng 15,0 m², WC 1,80 × 1,80 m, phù hợp con lớn.


03 Hai WC xếp trên WC master để rút ngắn ống cấp thoát và hộp kỹ thuật.

04 Ô cửa đầu-cuối nhà và giếng trời cầu thang tạo thông gió chéo.

03 / ROOF

TẦNG TUM

PHÒNG THỜ · SÂN THƯỢNG

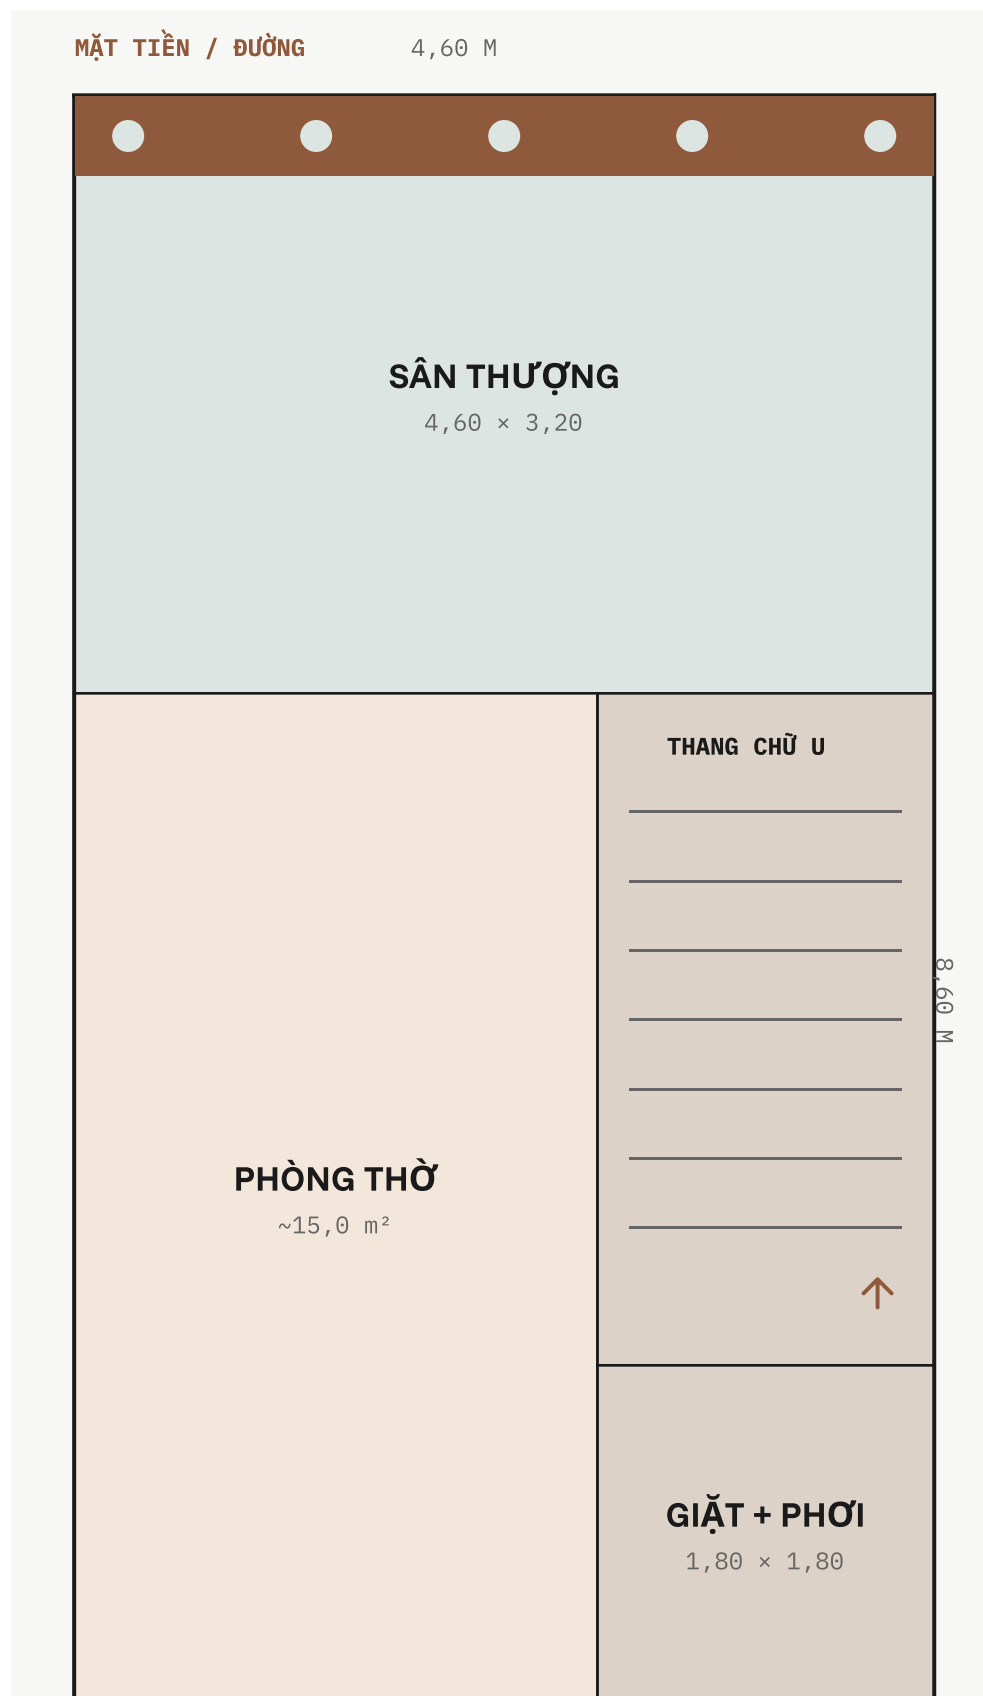

01 Sân thượng trước sâu 3,20 m, bố trí cây xanh, ghế nghỉ và pergola nhẹ.

02 Phòng thờ đặt sau sân, hướng bàn thờ nhìn về mặt tiền, có cửa lùa.

03 Kho giặt-phơi phía sau, tách khỏi phòng thờ bằng cửa kín và cây đệm.


04 Mái kính mở trên thang hỗ trợ hiệu ứng ống khói và thoát nhiệt ban đêm.

MẶT ĐỨNG & THÔNG THOÁNG

NGÔN NGỮ HIỆN ĐẠI · THÔNG GIÓ THỤ ĐỘNG


A / ELEVATION

MẶT ĐỨNG HIỆN ĐẠI

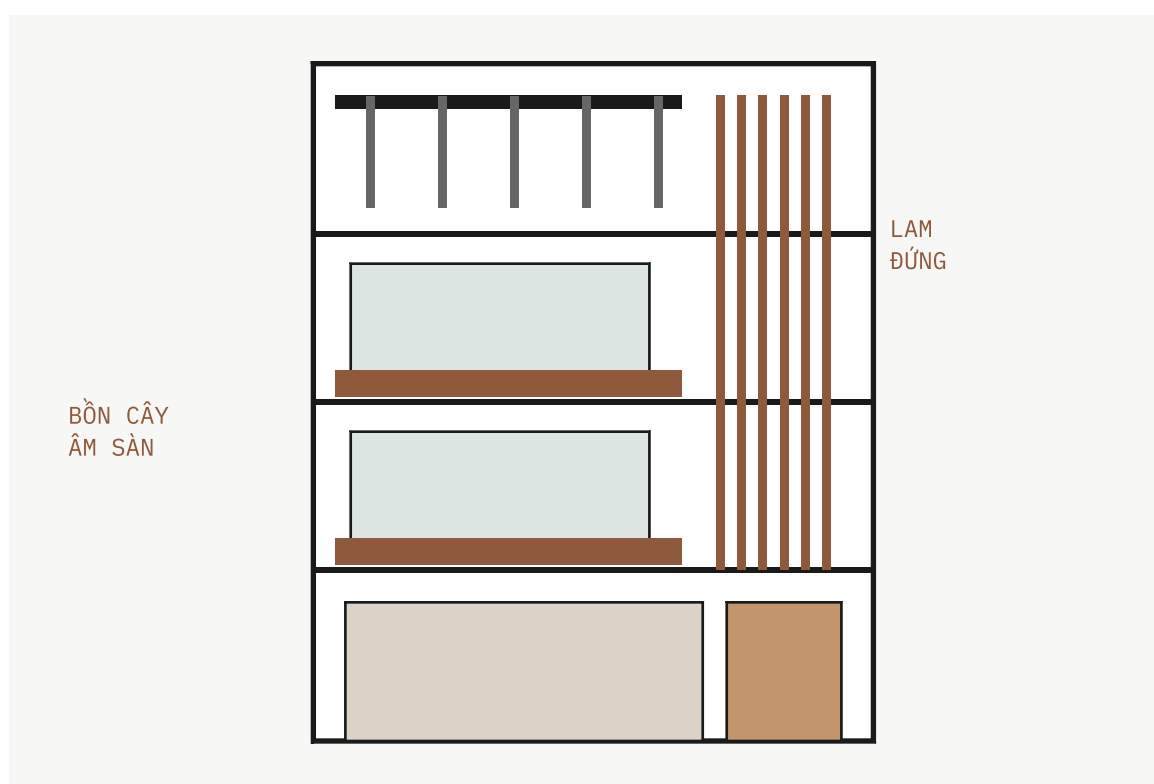


B / SECTION

ĐỐI LƯU QUA LỐI THANG

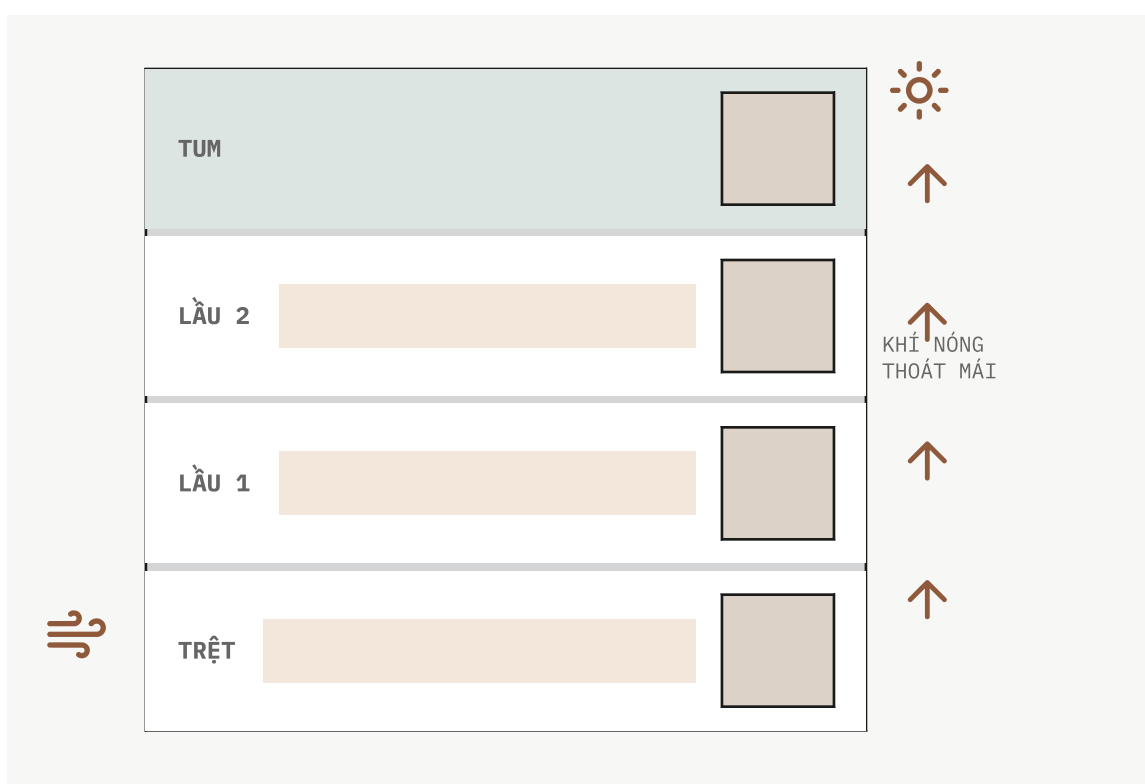

C / MATERIAL

BẢNG VẬT LIỆU GỢI Ý

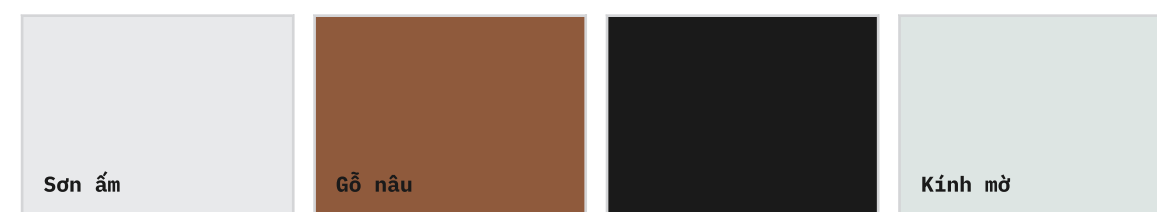

- Khung nhôm sơn tĩnh điện màu than, kính Low-E hoặc kính hộp.
- Lam đứng giả gỗ/nhôm giúp giảm nắng xiên và tăng riêng tư.
- Sàn gara chống trượt, có rãnh thu nước và quạt hút khí cưỡng bức.
- Cây bản địa ít rụng lá; tuổi nhỏ giọt và chống thấm bồn cây độc lập.

≈ 137 m²

SÀN KÍN ƯỚC TÍNH

3 sàn đầy đủ + phần phòng tum; chưa gồm sân thượng.

0,85–0,90 m

BỀ RỘNG VẾ THANG

Cần chốt theo kết cấu, lan can và quy chuẩn địa phương.

01 TRỤC UỐT

MEP GỌN

WC các tầng xếp chồng, hộp kỹ thuật đặt cuối nhà.

TRƯỚC KHI TRIỂN KHAI HỒ SƠ KỸ THUẬT

- Hướng khu đất, khoảng lùi trước/sau, nhà liền kề và vị trí cửa sổ được phép mở.
- Kích thước thực tế của ô tô, bán kính quay đầu và cao độ vỉa hè.
- Giải pháp móng, cột, dầm và vị trí hộp kỹ thuật sau khảo sát hiện trạng.
- Thông gió gara, chống cháy, chống thấm sân thượng và yêu cầu xin phép địa phương.